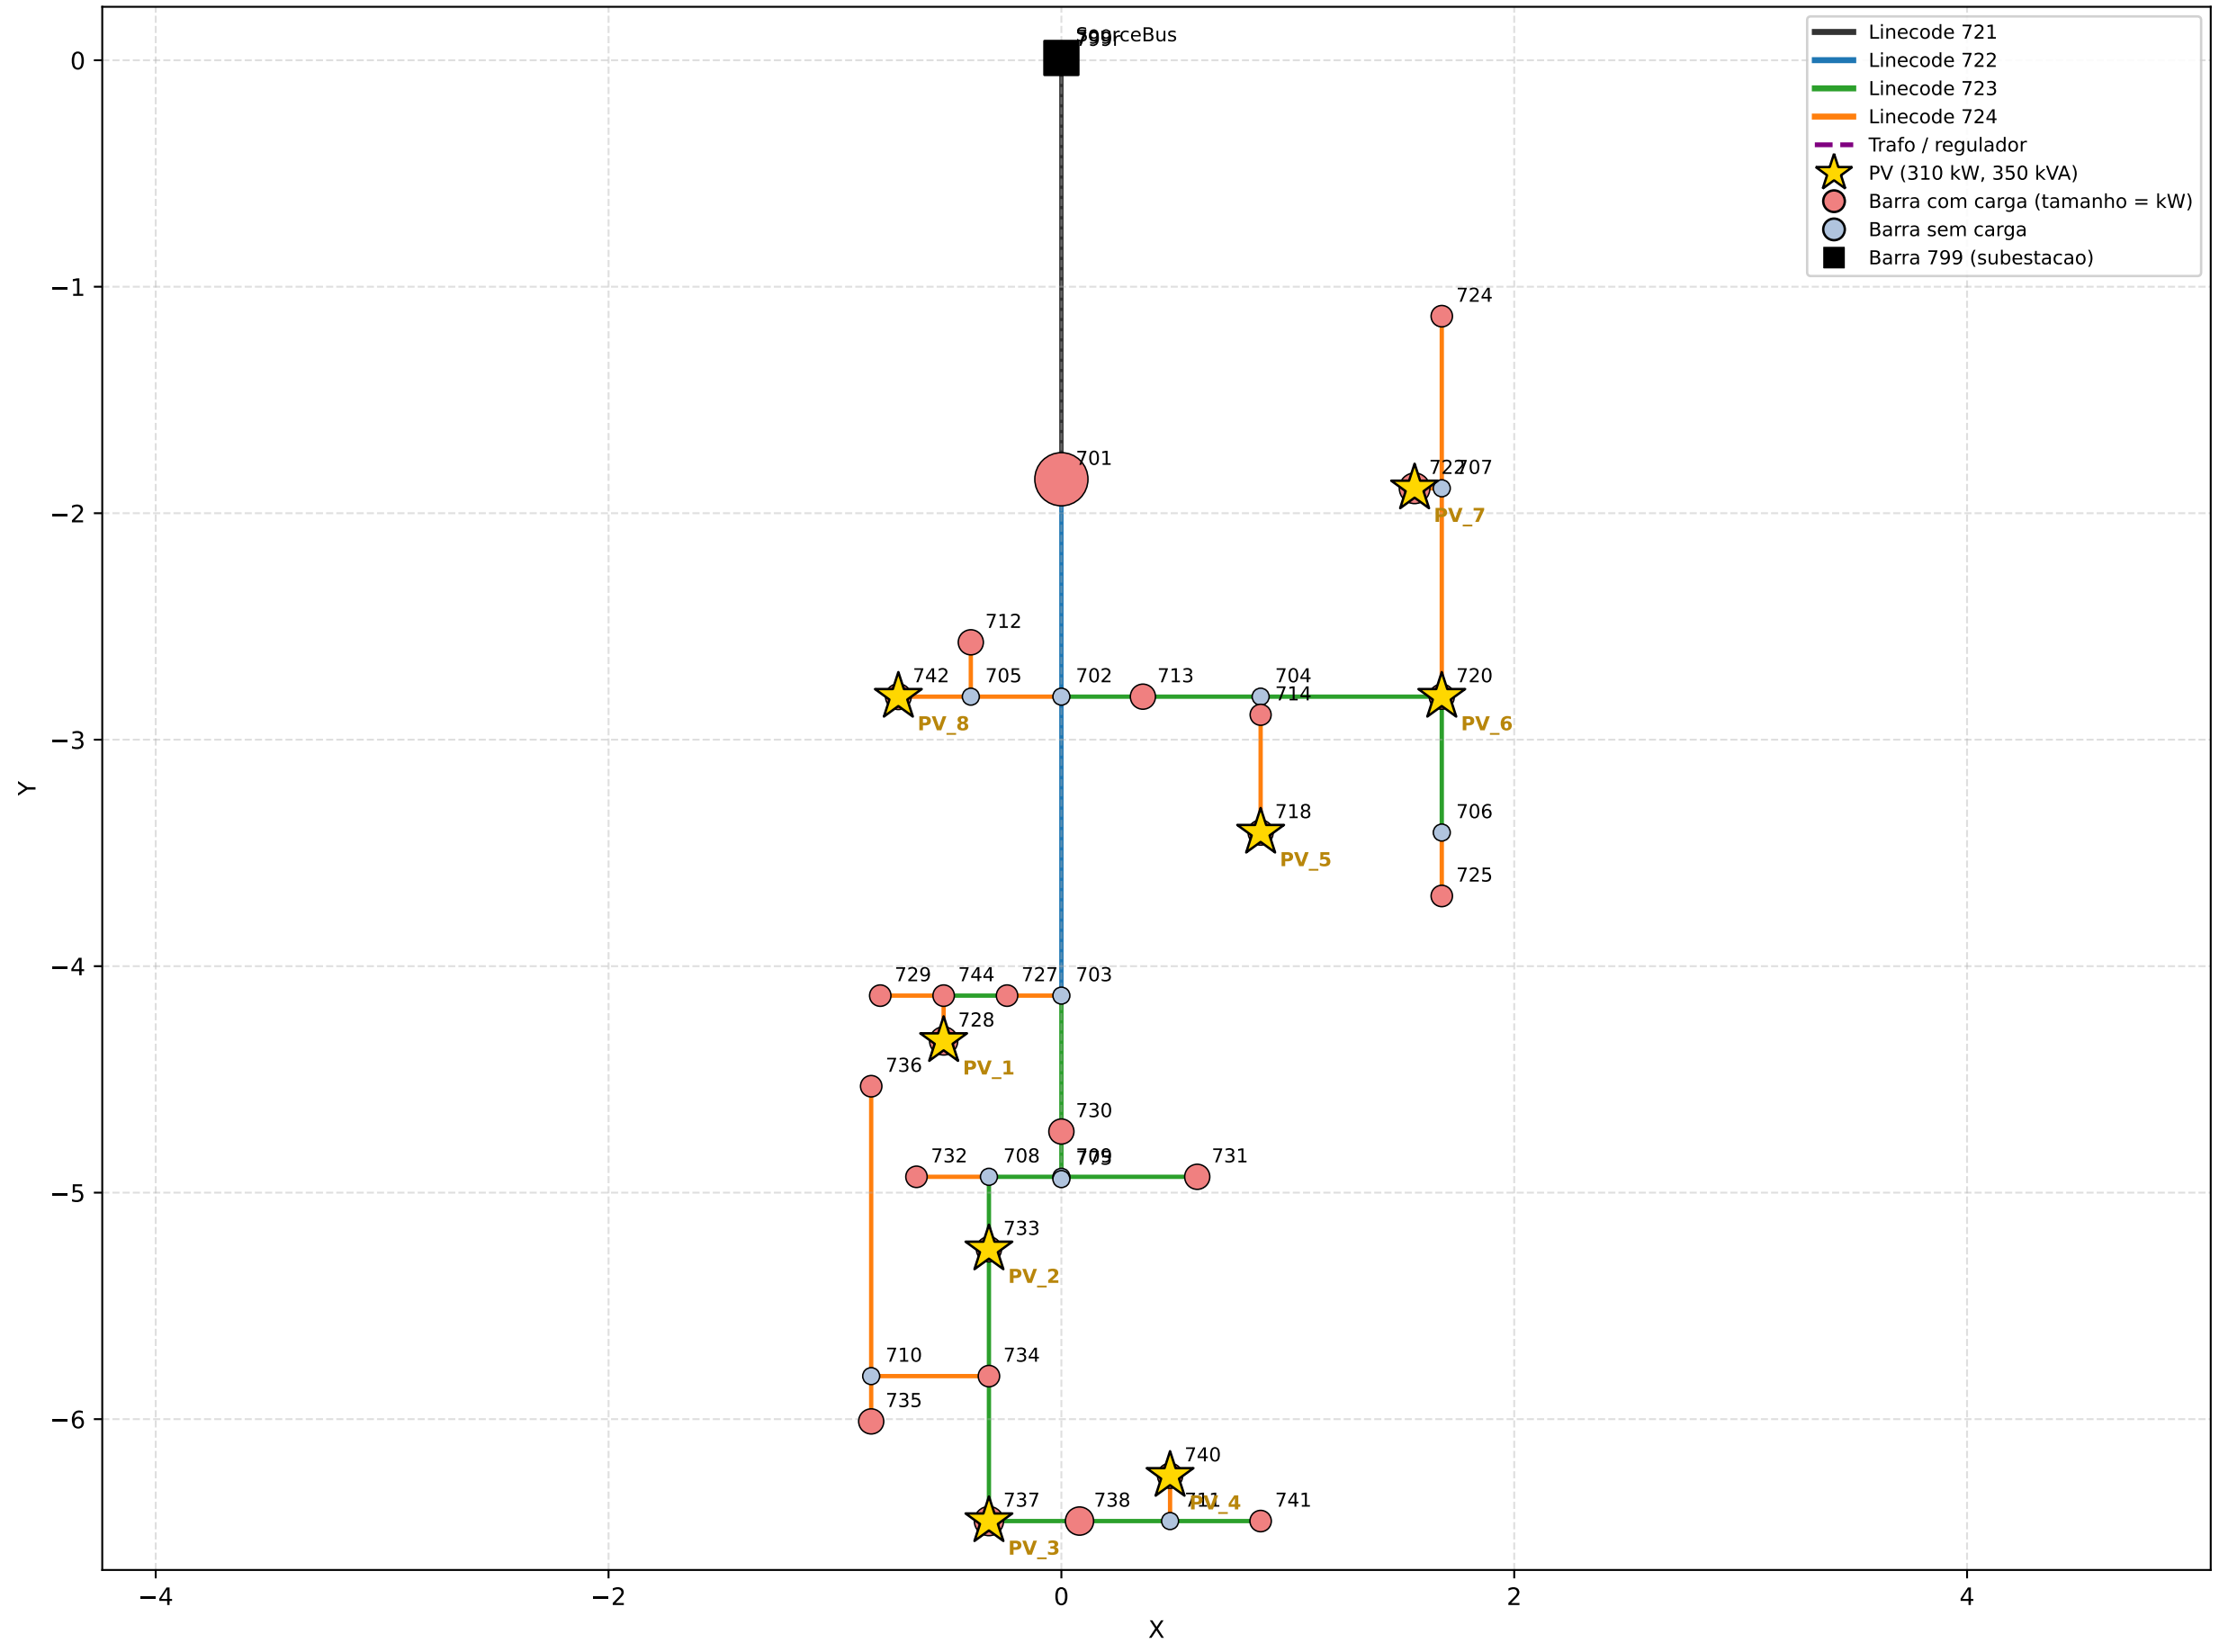
IEEE 37 Barras: topologia, cargas e PVs (8 x 310 kW)
Linecode 721
Linecode 722
Linecode 723
Linecode 724
Trafo / regulador
PV (310 kW, 350 kVA)
Barra com carga (tamanho = kW)
Barra sem carga
Barra 799 (subestacao)
799
701
724
707
PV_7
712
742
705
702
713
704
714
720
PV_8
PV_6
718
PV_5
706
725
729
744
727
703
728
736
PV_1
730
732
708
709
731
733
PV_2
710
734
735
740
737
738
741
PV_4
PV_3
X
Y